



RZUT STANU ISTNIEJĄCEGO
skala 1:50

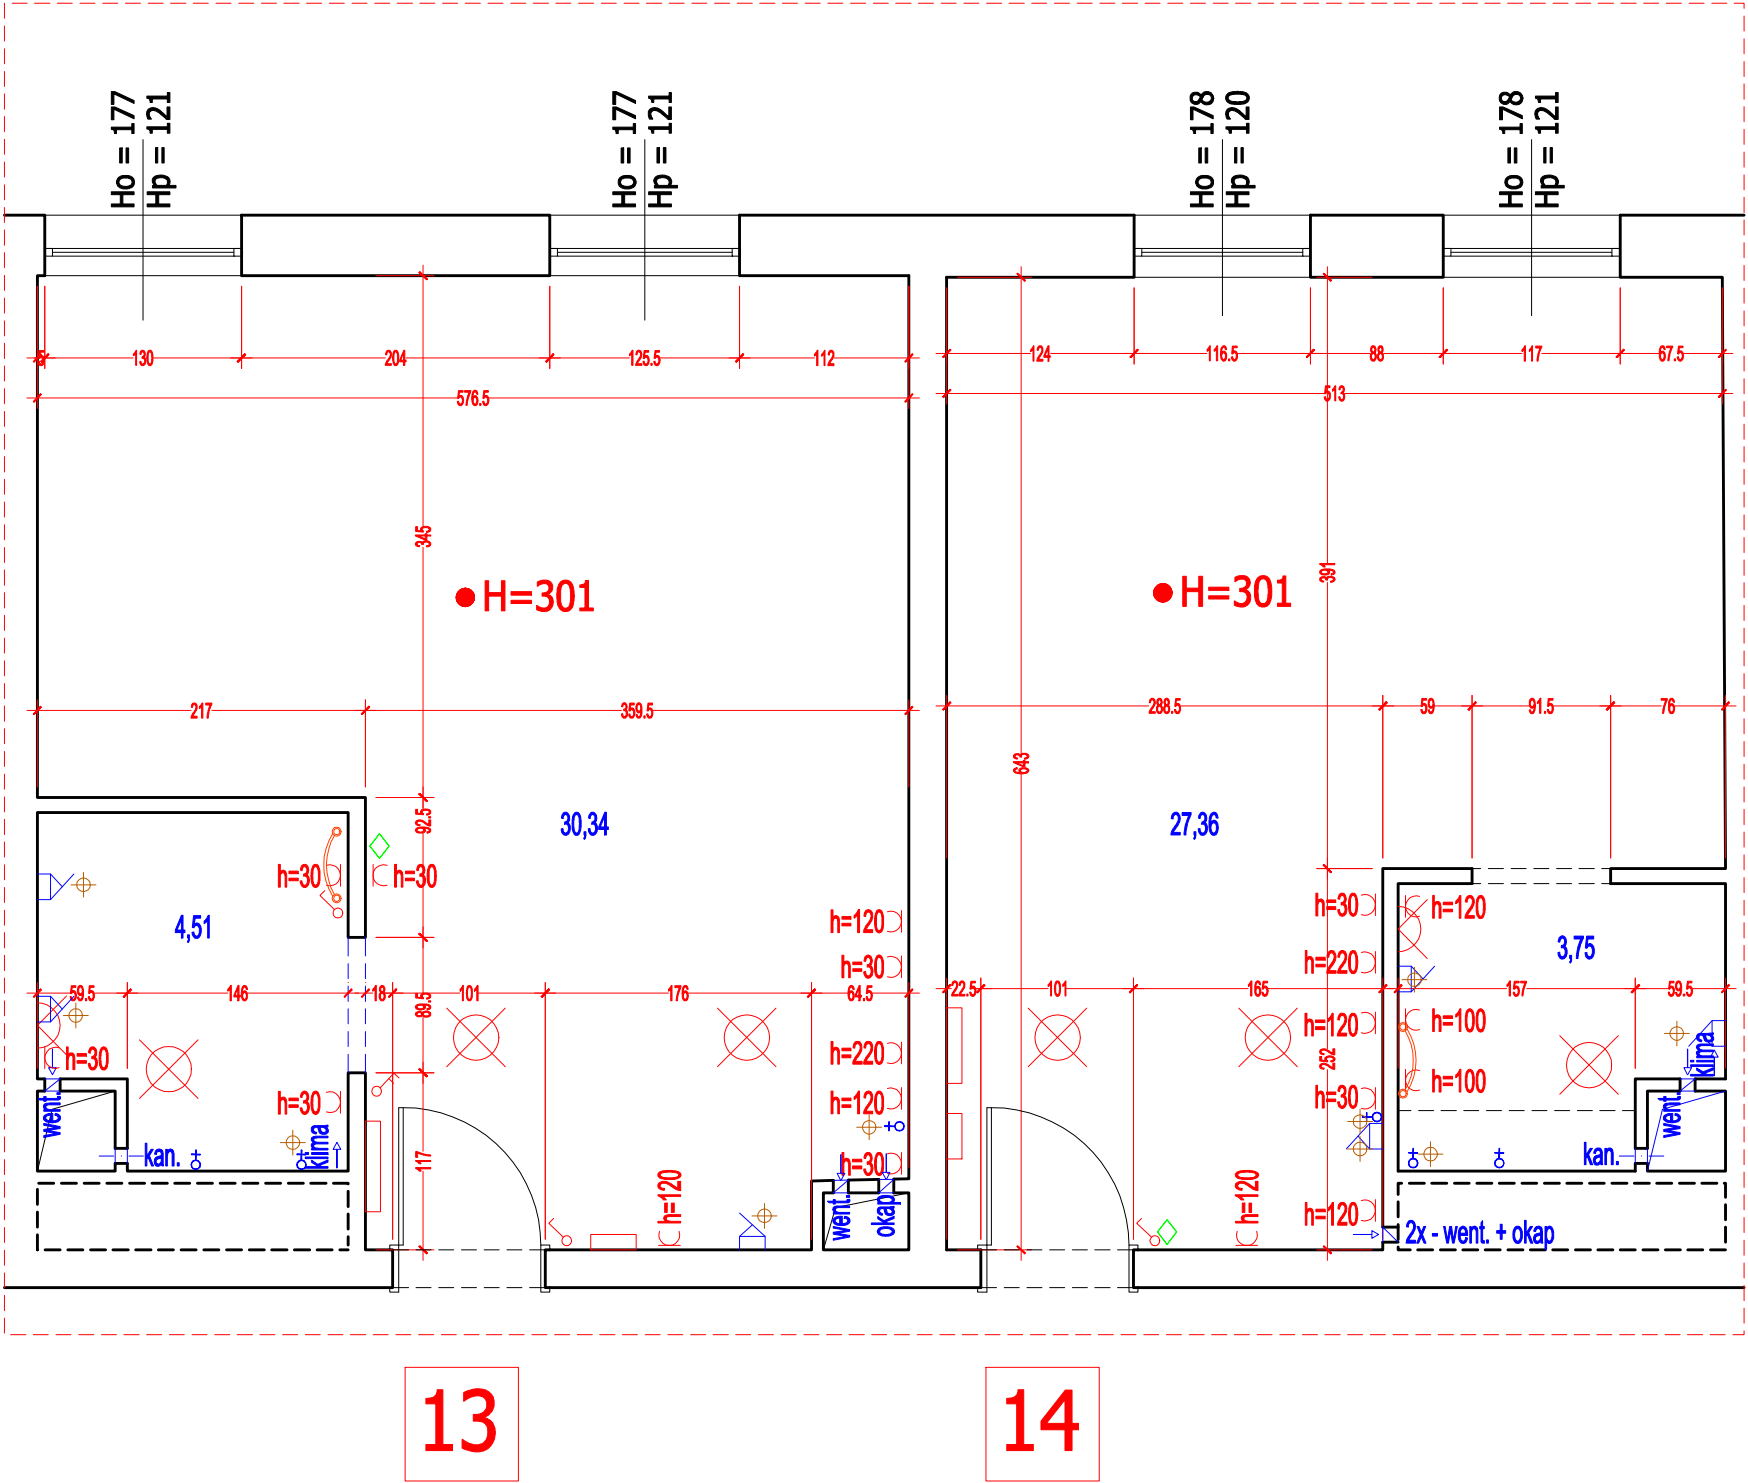


TEMAT	ARANŻACJA LOKALI MIESZKALNYCH	Pracownia Projektowa MAK A ul. Odrowąża 28/8, 30-009 Kraków 609-475-980	
ADRES	UL. KALWARYSKA 14 KRAKÓW, M. 13 / 14		
INWESTOR	PRYWATNY		
DATA	05.2026		
BRANŻA	ARANŻACJA WNIĘTRZ	AUTOR	SPRAWDZIŁ
A1	RZUT STANU ISTNIEJĄCEGO	ARCH. M. KAPOLKA, UPR. NR 083/17	
SKALA	1:50		

RZUT STANU PROJEKTOWANEGO
skala 1:50

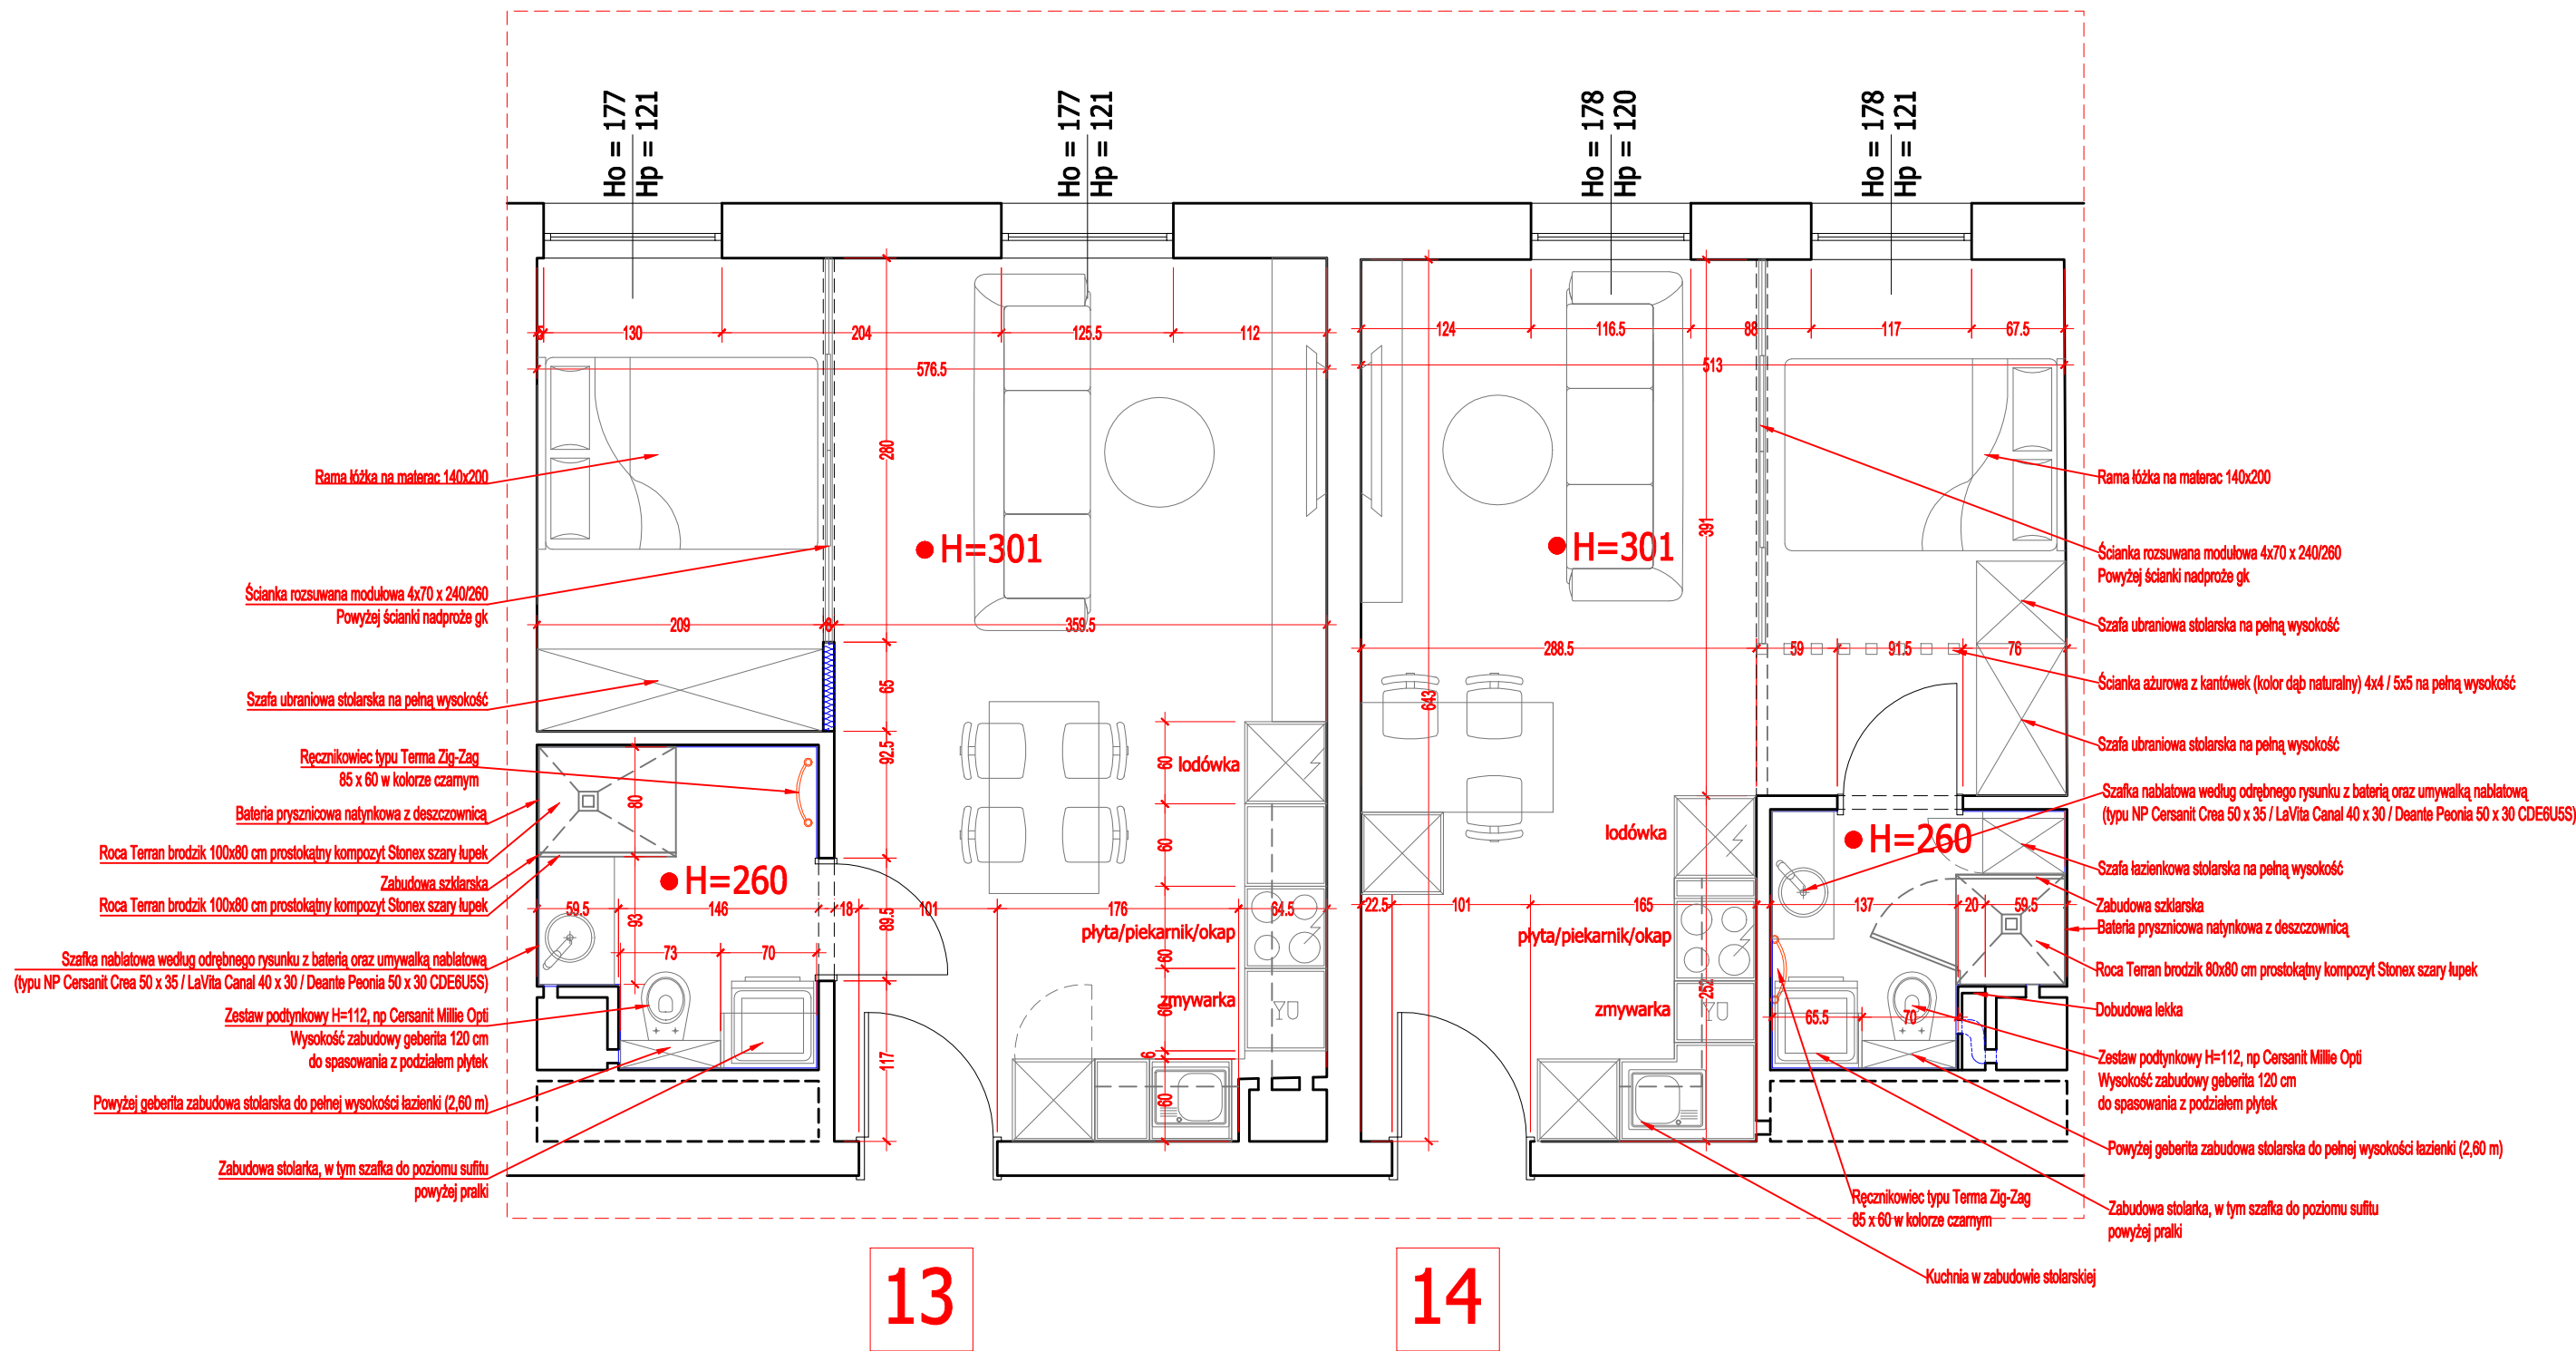

TEMAT	ARANŻACJA LOKALI MIESZKALNYCH	Pracownia Projektowa MAK Architekti Maciej Andrzej Kapoła ul. Odrowąża 28/8, 30-009 Kraków 609-475-980	
ADRES	UL. KALWARYSKA 14 KRAKÓW, M. 13 / 14		
INWESTOR	PRYWATNY		
DATA	05.2026		
BRANŻA	ARANŻACJA WNIĘTRZ	AUTOR	ARCH. M. KAPOŁKA, UP.R. NR 083/17
A2	RZUT STANU PROJEKTOWANEGO	SPRAWDZIŁ	
SKALA	1:50		


RZUT ROZBUDOWY INSTALACJI
skala 1:50

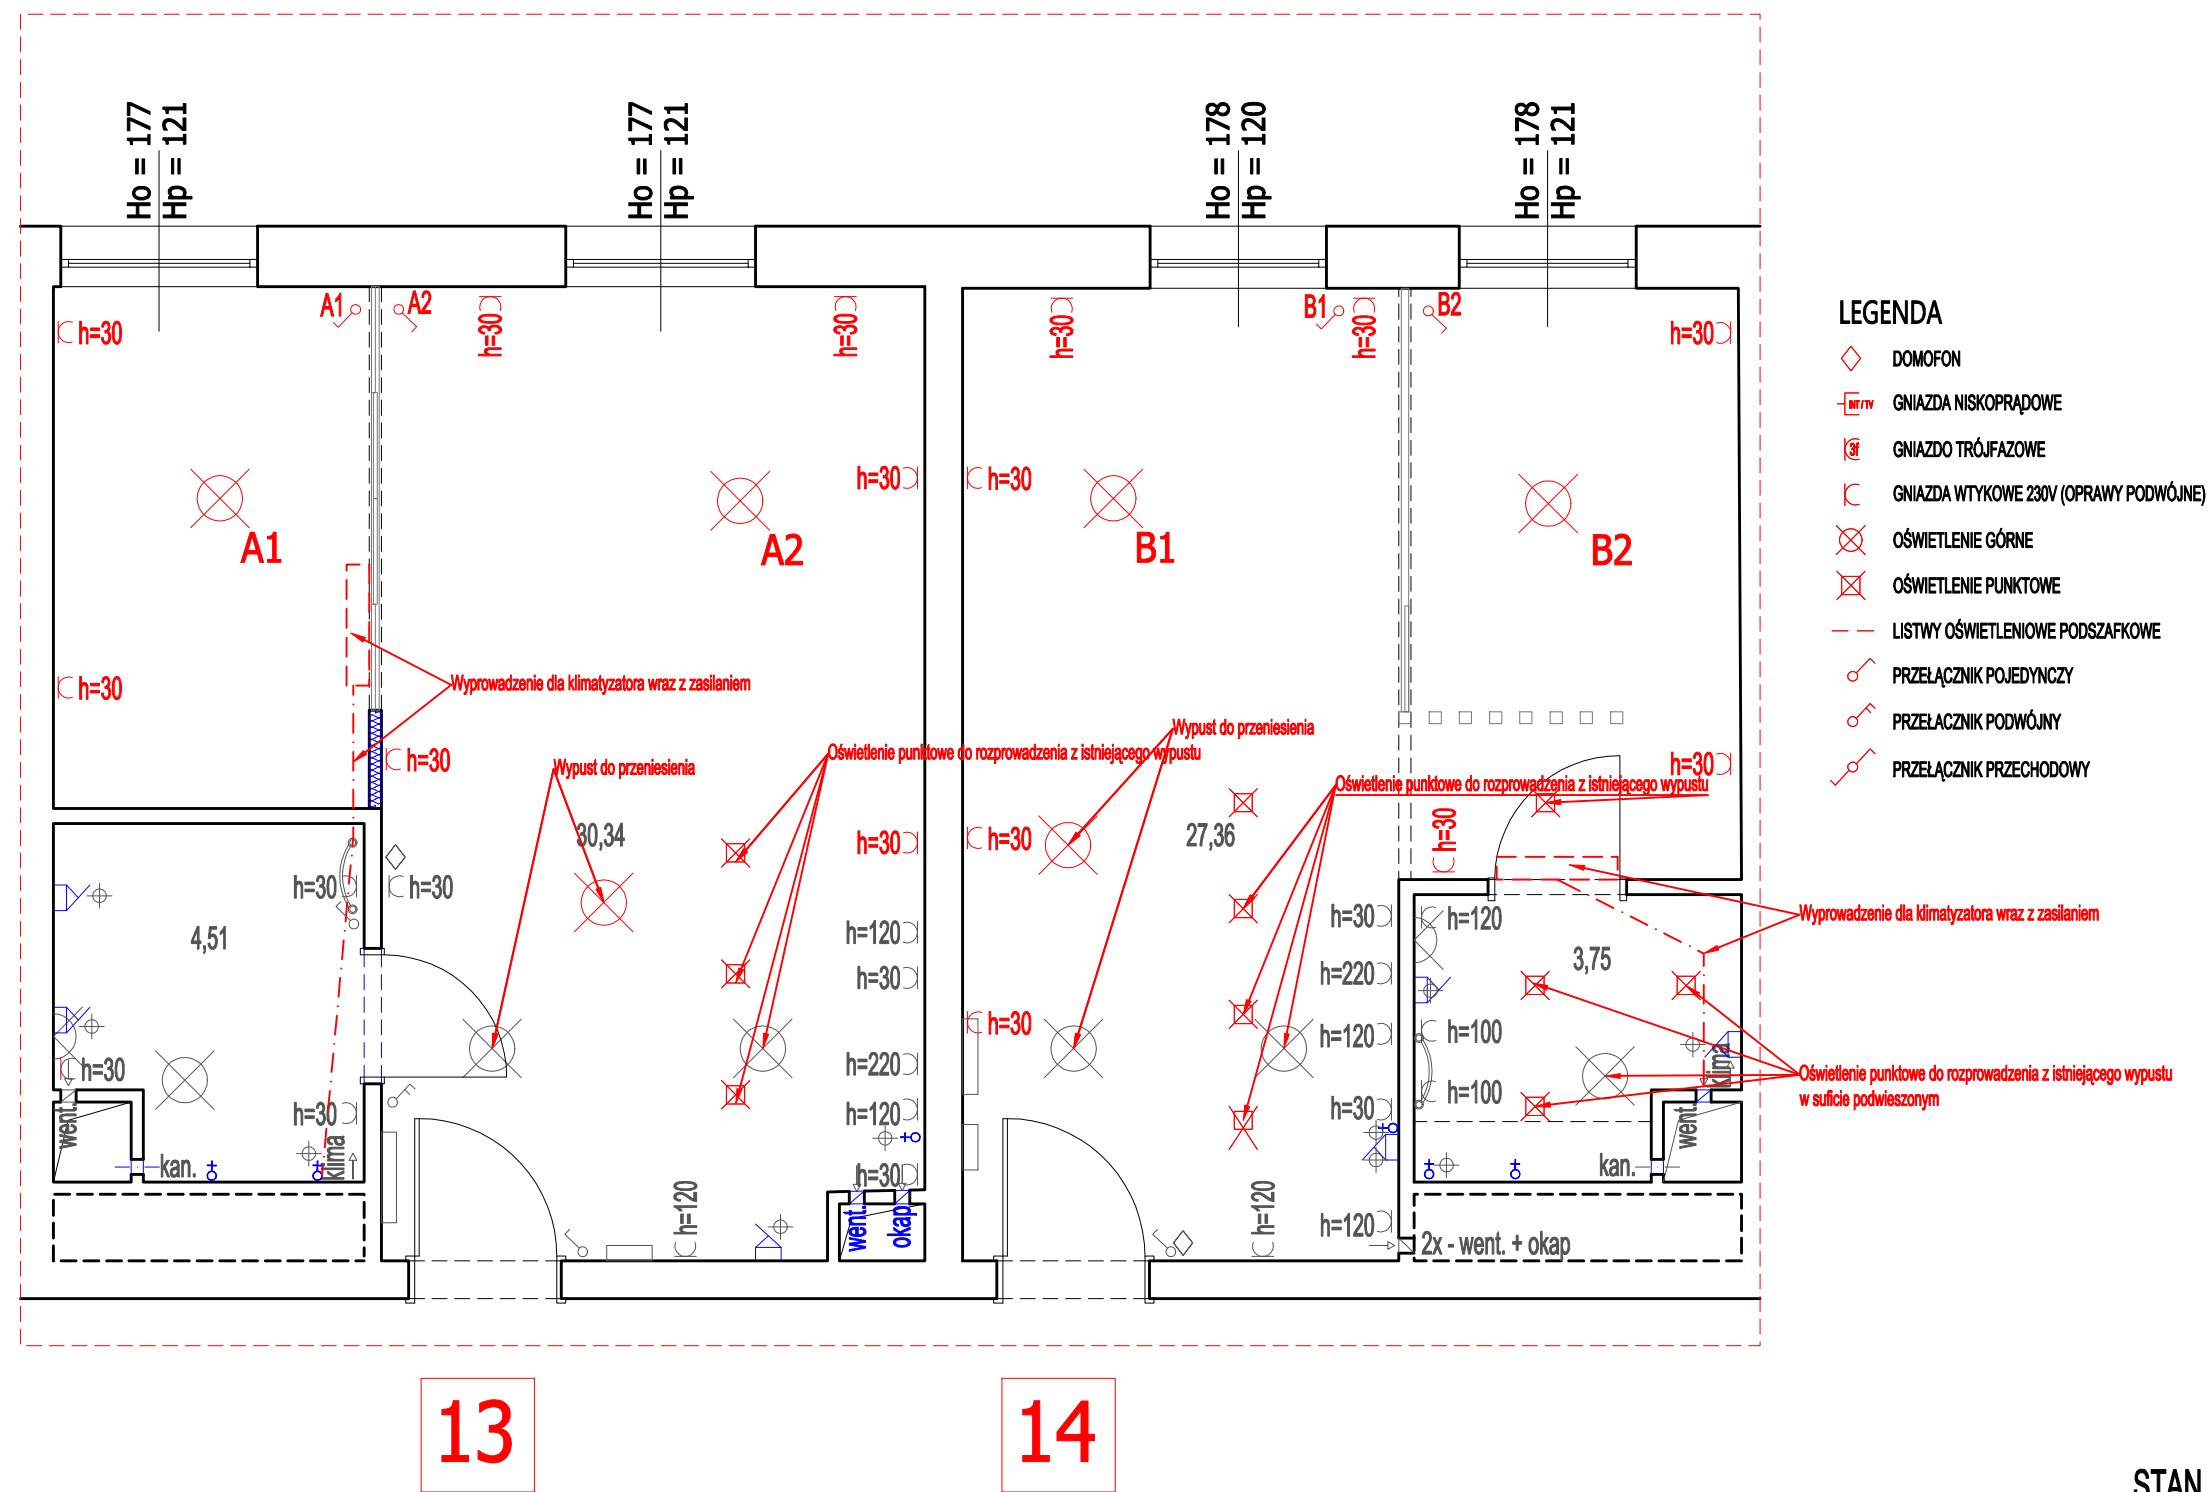

UWAGA!
BRAK ZMIAN W INSTALACJI WOD-KAN
ELEMENTY ISTNIEJĄCE INSTALACJI ELEKTRYCZNYCH OZNACZONO KOLOREM SZARYM
ELEMENTY NOWOPROJEKTOWANE OZNACZONO KOLOREM CZERWONYM

TEMAT	ARANŻACJA LOKALI MIESZKALNYCH	STAN NA: 14.05.2026 Pracownia Projektowa MAK Architekt Maciej Andrzej Kapoła ul. Odrowąża 28/8, 30-009 Kraków 609-475-980 A M A K	
ADRES	UL. KALWARYSKA 14 KRAKÓW, M. 13 / 14		
INWESTOR	PRYWATNY		
DATA	05.2026		
BRANŻA	ARANŻACJA WNIĘTRZ	AUTOR	SPRAWDZIŁ
A3	RZUT ROZBUDOWY INSTALACJI	ARCH. M. KAPOŁA, UPR. NR 083/17	
SKALA			
1:50			

RZUT SUFITÓW PODWIESZONYCH
skala 1:50

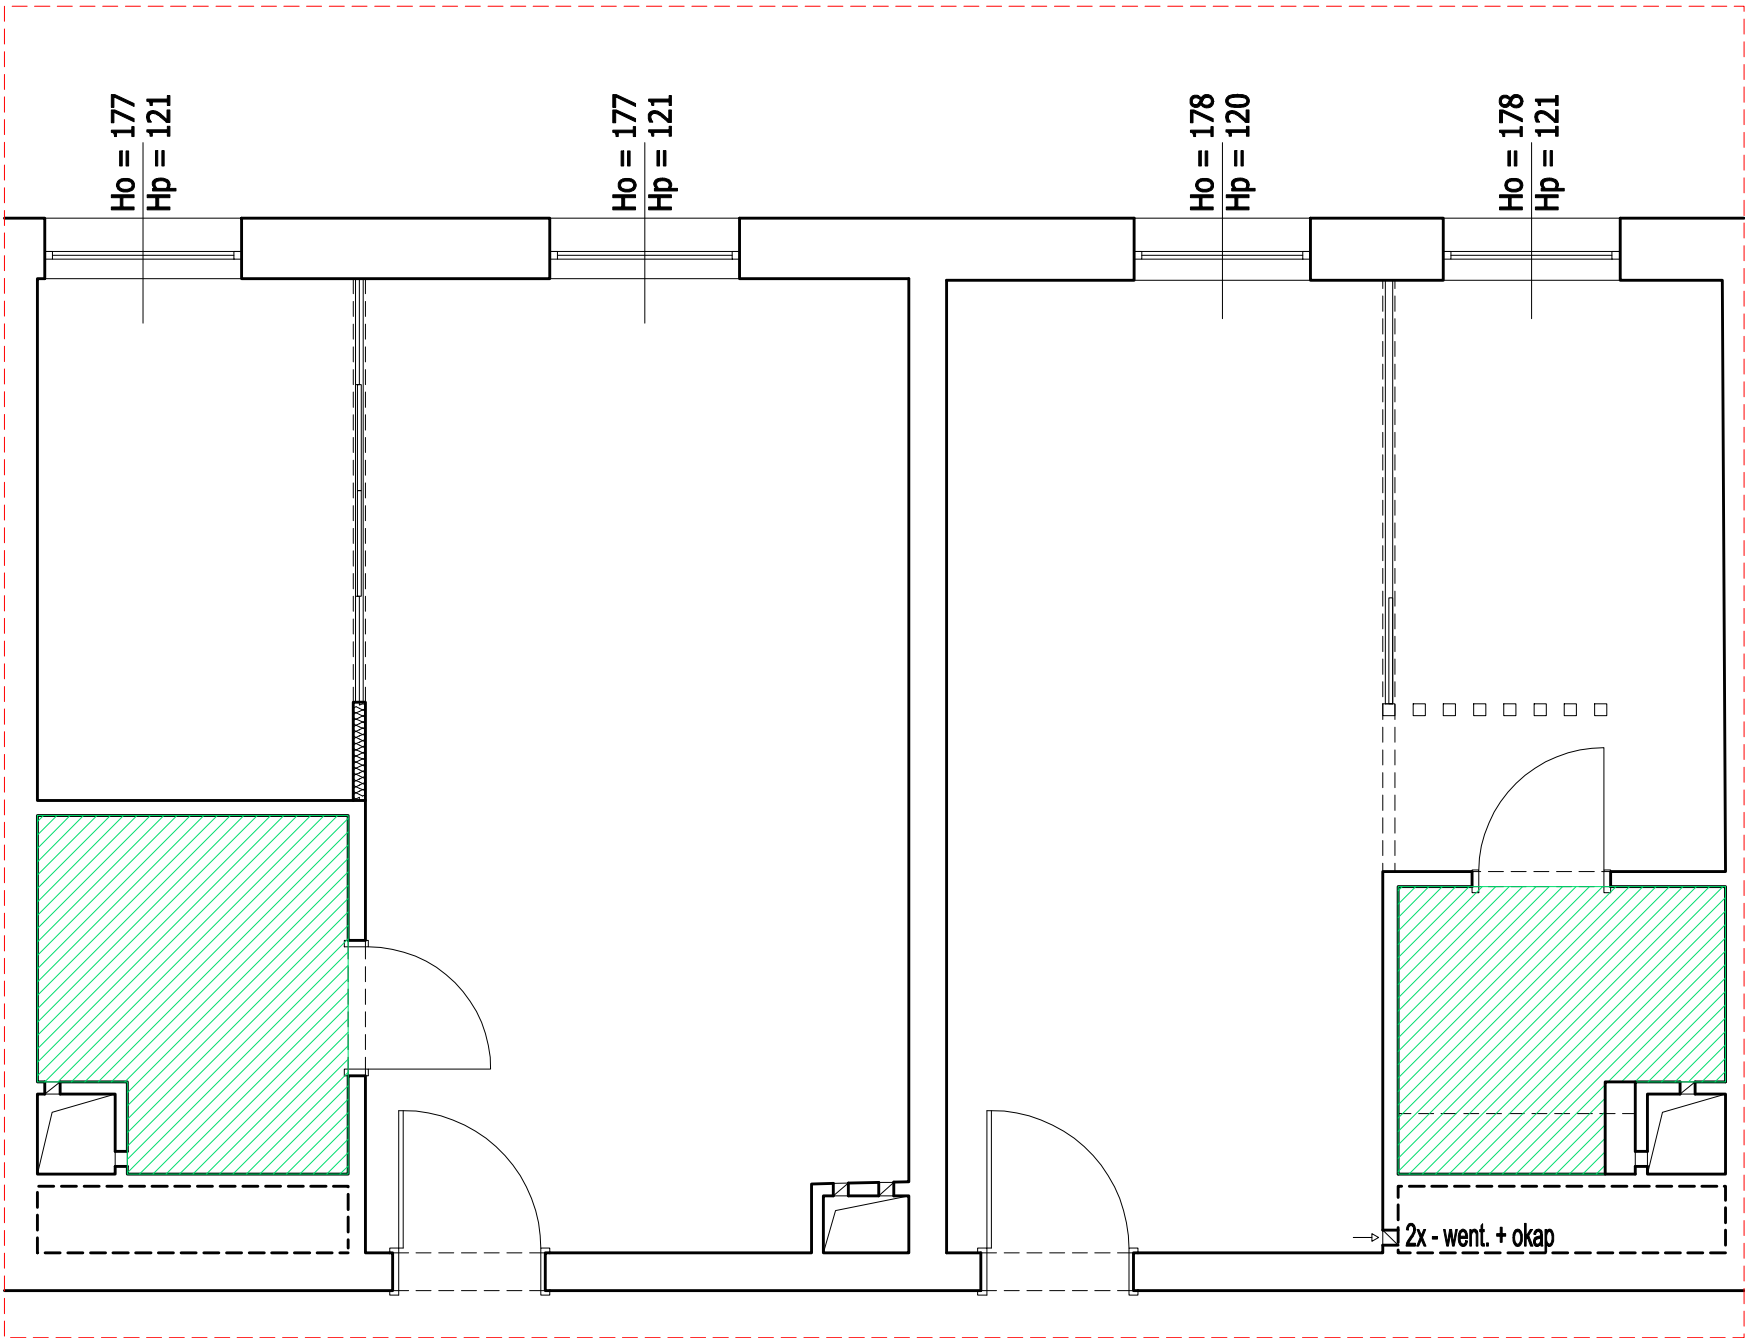


LEGENDA

 SUFIT GK, OBNIŻONY DO WYS. +2,60

TEMAT	ARANŻACJA LOKALI MIESZKALNYCH		 Pracownia Projektowa MAKKA Architekti Maciej Andrzej Kapoła ul. Odrowęża 28/8, 30-009 Kraków 609-475-980	
ADRES	UL. KALWARYSKA 14 KRAKÓW, M. 13 / 14			
INWESTOR	PRYWATNY			
DATA	05.2026			
BRANŻA	ARANŻACJA WNIĘTRZ.		AUTOR	SPRAWDZIŁ
A4	RZUT SUFITÓW PODWIESZONYCH		ARCH. M. KAPOŁKA, UPR. NR 083/17	
SKALA				
1:50				

RZUT PODŁÓG
skala 1:50

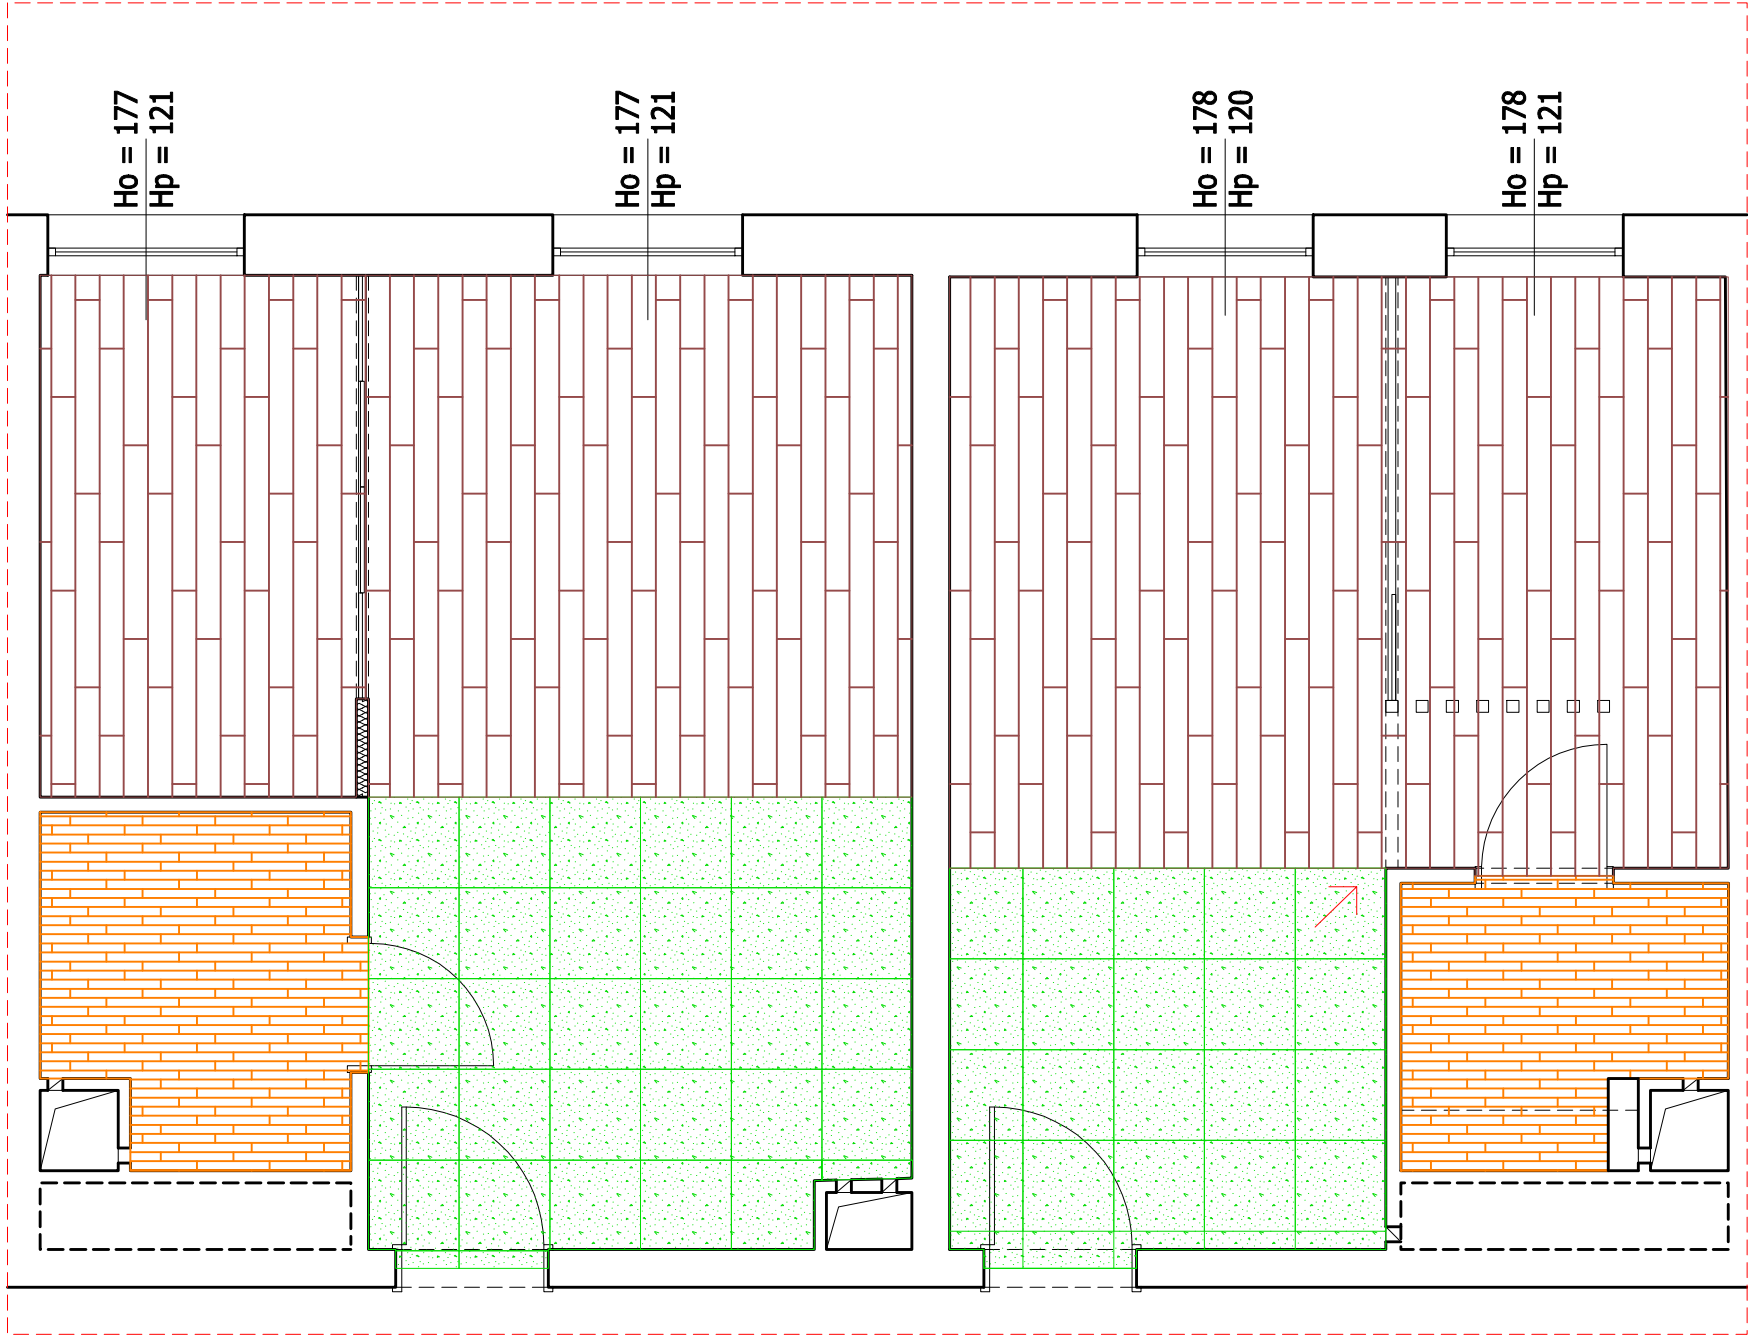


LEGENDA			
SYMBOL	OPIS	ILOŚĆ [m²]	ILOŚĆ + zapas [m²]
	PANEL LAMINOWANY Quick-Step Capture Dąb szczotkowany naturalny ciepły SIG4762	40,00	45,00
	PLYTKA GRESOWA 60x60 CM - PARADYŻ U117 (Ennis) Light Grey Gres Szkl. Rekt. Półpoker 59,8x59,8	18,00	20,00
	PLYTKA GRESOWA DREWNOPODOBNA 10x60 - PARADYŻ FREELAND GOLD	8,50	10,00

DLA PANELI ORAZ PLYTEK W CZĘŚCI PRZEDPOKOJOWEJ ZASTOSOWAĆ NALEŻY COKOLY SYSTEMOWE LUB W PRZYPADKU BRAKU DOPASOWAĆ KOLORYSTYCZNIE STOSOWANY MATERIAŁ. ŁAZIENKI WYKONCZANIE PLYTKAMI CERAMICZNYMI NA PEŁNĄ WYSOKOŚĆ.

TEMAT	ARANŻACJA LOKALI MIESZKALNYCH			Pracownia Projektowa MAK A Architekt Maciej Andrzej Kapołka ul. Odrowąża 28/8, 30-009 Kraków 609-475-980	
ADRES	UL. KALWARYSKA 14 KRAKÓW, M. 13 / 14				
INWESTOR	PRYWATNY				
DATA	05.2026				
BRANŻA	ARANŻACJA WNEŹRZ		AUTOR	SPRAWDZIŁ	
A5	RZUT PODŁÓG		ARCH. M. KAPOŁKA, UP.R. NR 083/17		
SKALA					
1:50					

RZUT WYKOŃCZEŃ ŚCIAN
skala 1:50

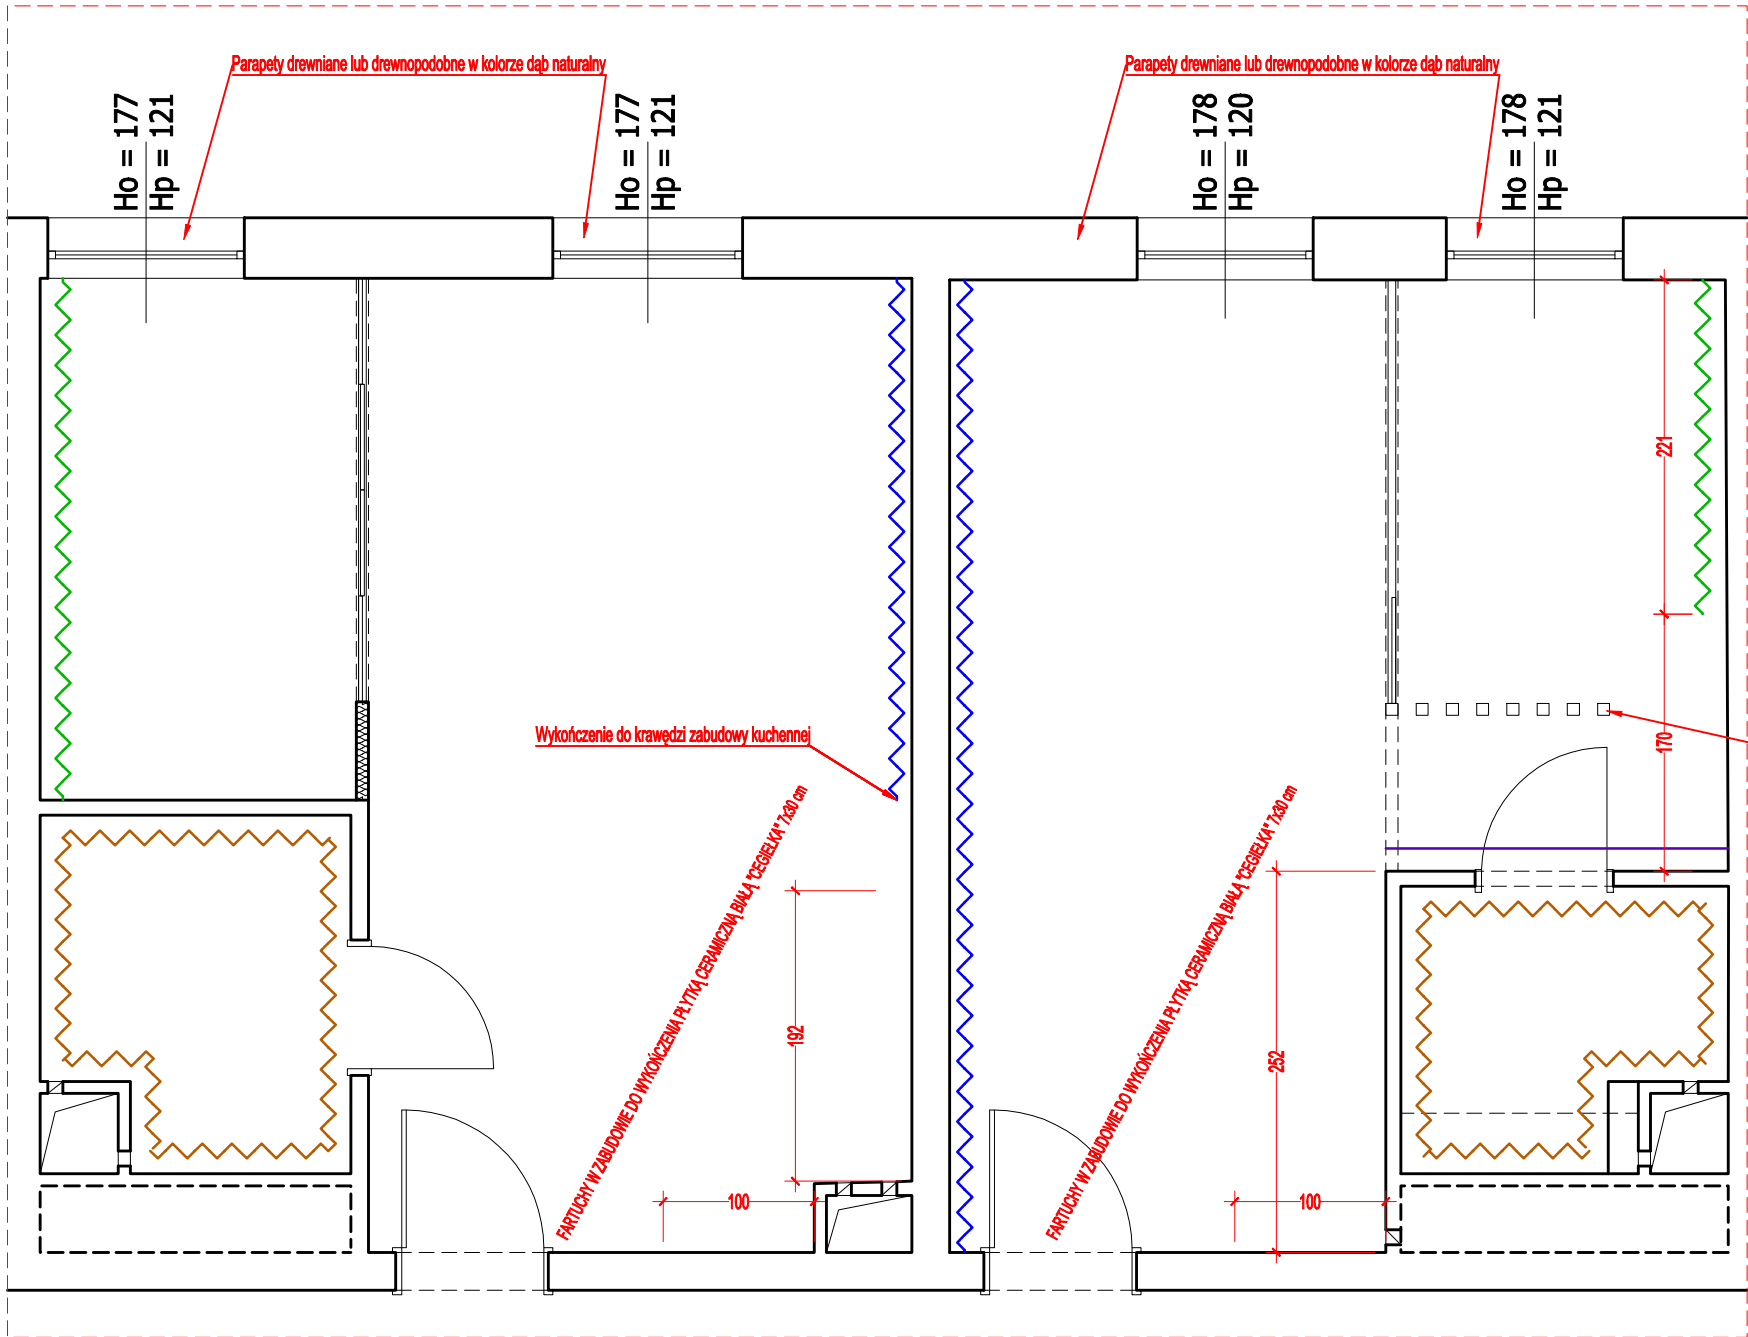

LEGENDA	
SYMBOL	OPIS
	ŚCIANY MALOWANE NA KOLOR JASNOBEŻOWY/BIAŁY - REF. TIKKURILA G503 "CALLA", NCS 0402-Y28R
	ŚCIANY MALOWANE NA KOLOR ANTRACYTOWY - RAL 7016
	ŚCIANY DO WYKOŃCZENIA BETONEM ARCHITEKTONICZNYM / FARBĄ STRUKTURALNĄ TYPU "BETON ARCHITEKTONICZNY"
	ŚCIANY DO TAPETOWANIA
	ŚCIANY ŁAZIENEK DO WYKOŃCZENIA PŁYTKAMI CERAMICZNYMI NA PEŁNĄ WYSOKOŚĆ POMIESZCZENIA WEDŁUG RYSUNKÓW INDYWIDUALNYCH

TEMAT	ARANŻACJA LOKALI MIESZKALNYCH	Pracownia Projektowa MAKKA Architekti Maciej Andrzej Kapołka ul. Odrowąża 28/8, 30-009 Kraków 609-475-980 MAKKA	
ADRES	UL. KALWARYSKA 14 KRAKÓW, M. 13 / 14		
INWESTOR	PRYWATNY		
DATA	05.2026		
BRANŻA	ARANŻACJA WNIĘTRZ	AUTOR	SPRAWDZIŁ
A6	RZUT WYKOŃCZEŃ ŚCIAN	ARCH. M. KAPOŁKA, UPR. NR 083/17	
SKALA	1:50		